

Projekt	Sond
Bearbeiter	Halime Karanfil
Datum	03/04/2025
Blatt	Sond_01 1/4
Massstab	1:750



Legende

- Manhole
 - Pop
 - Dp
 - △ Duct_Joint
 - Adresspoint

Trench

- Bürgersteig
 - Garden Trench
 - Strasse
 - Strassenkreuzung
 - POP_Cluster
 - Dp_Cluster
 - Flurstck


OpenStreetMap

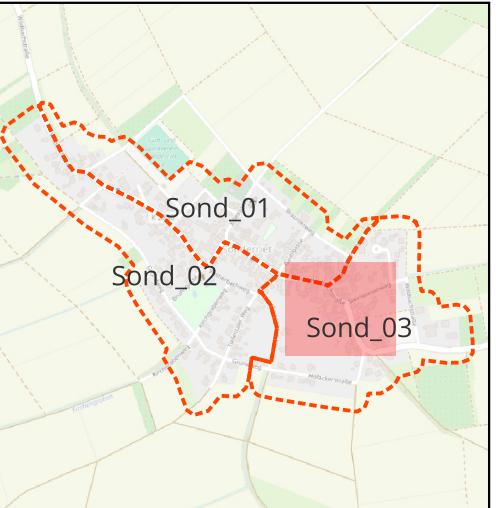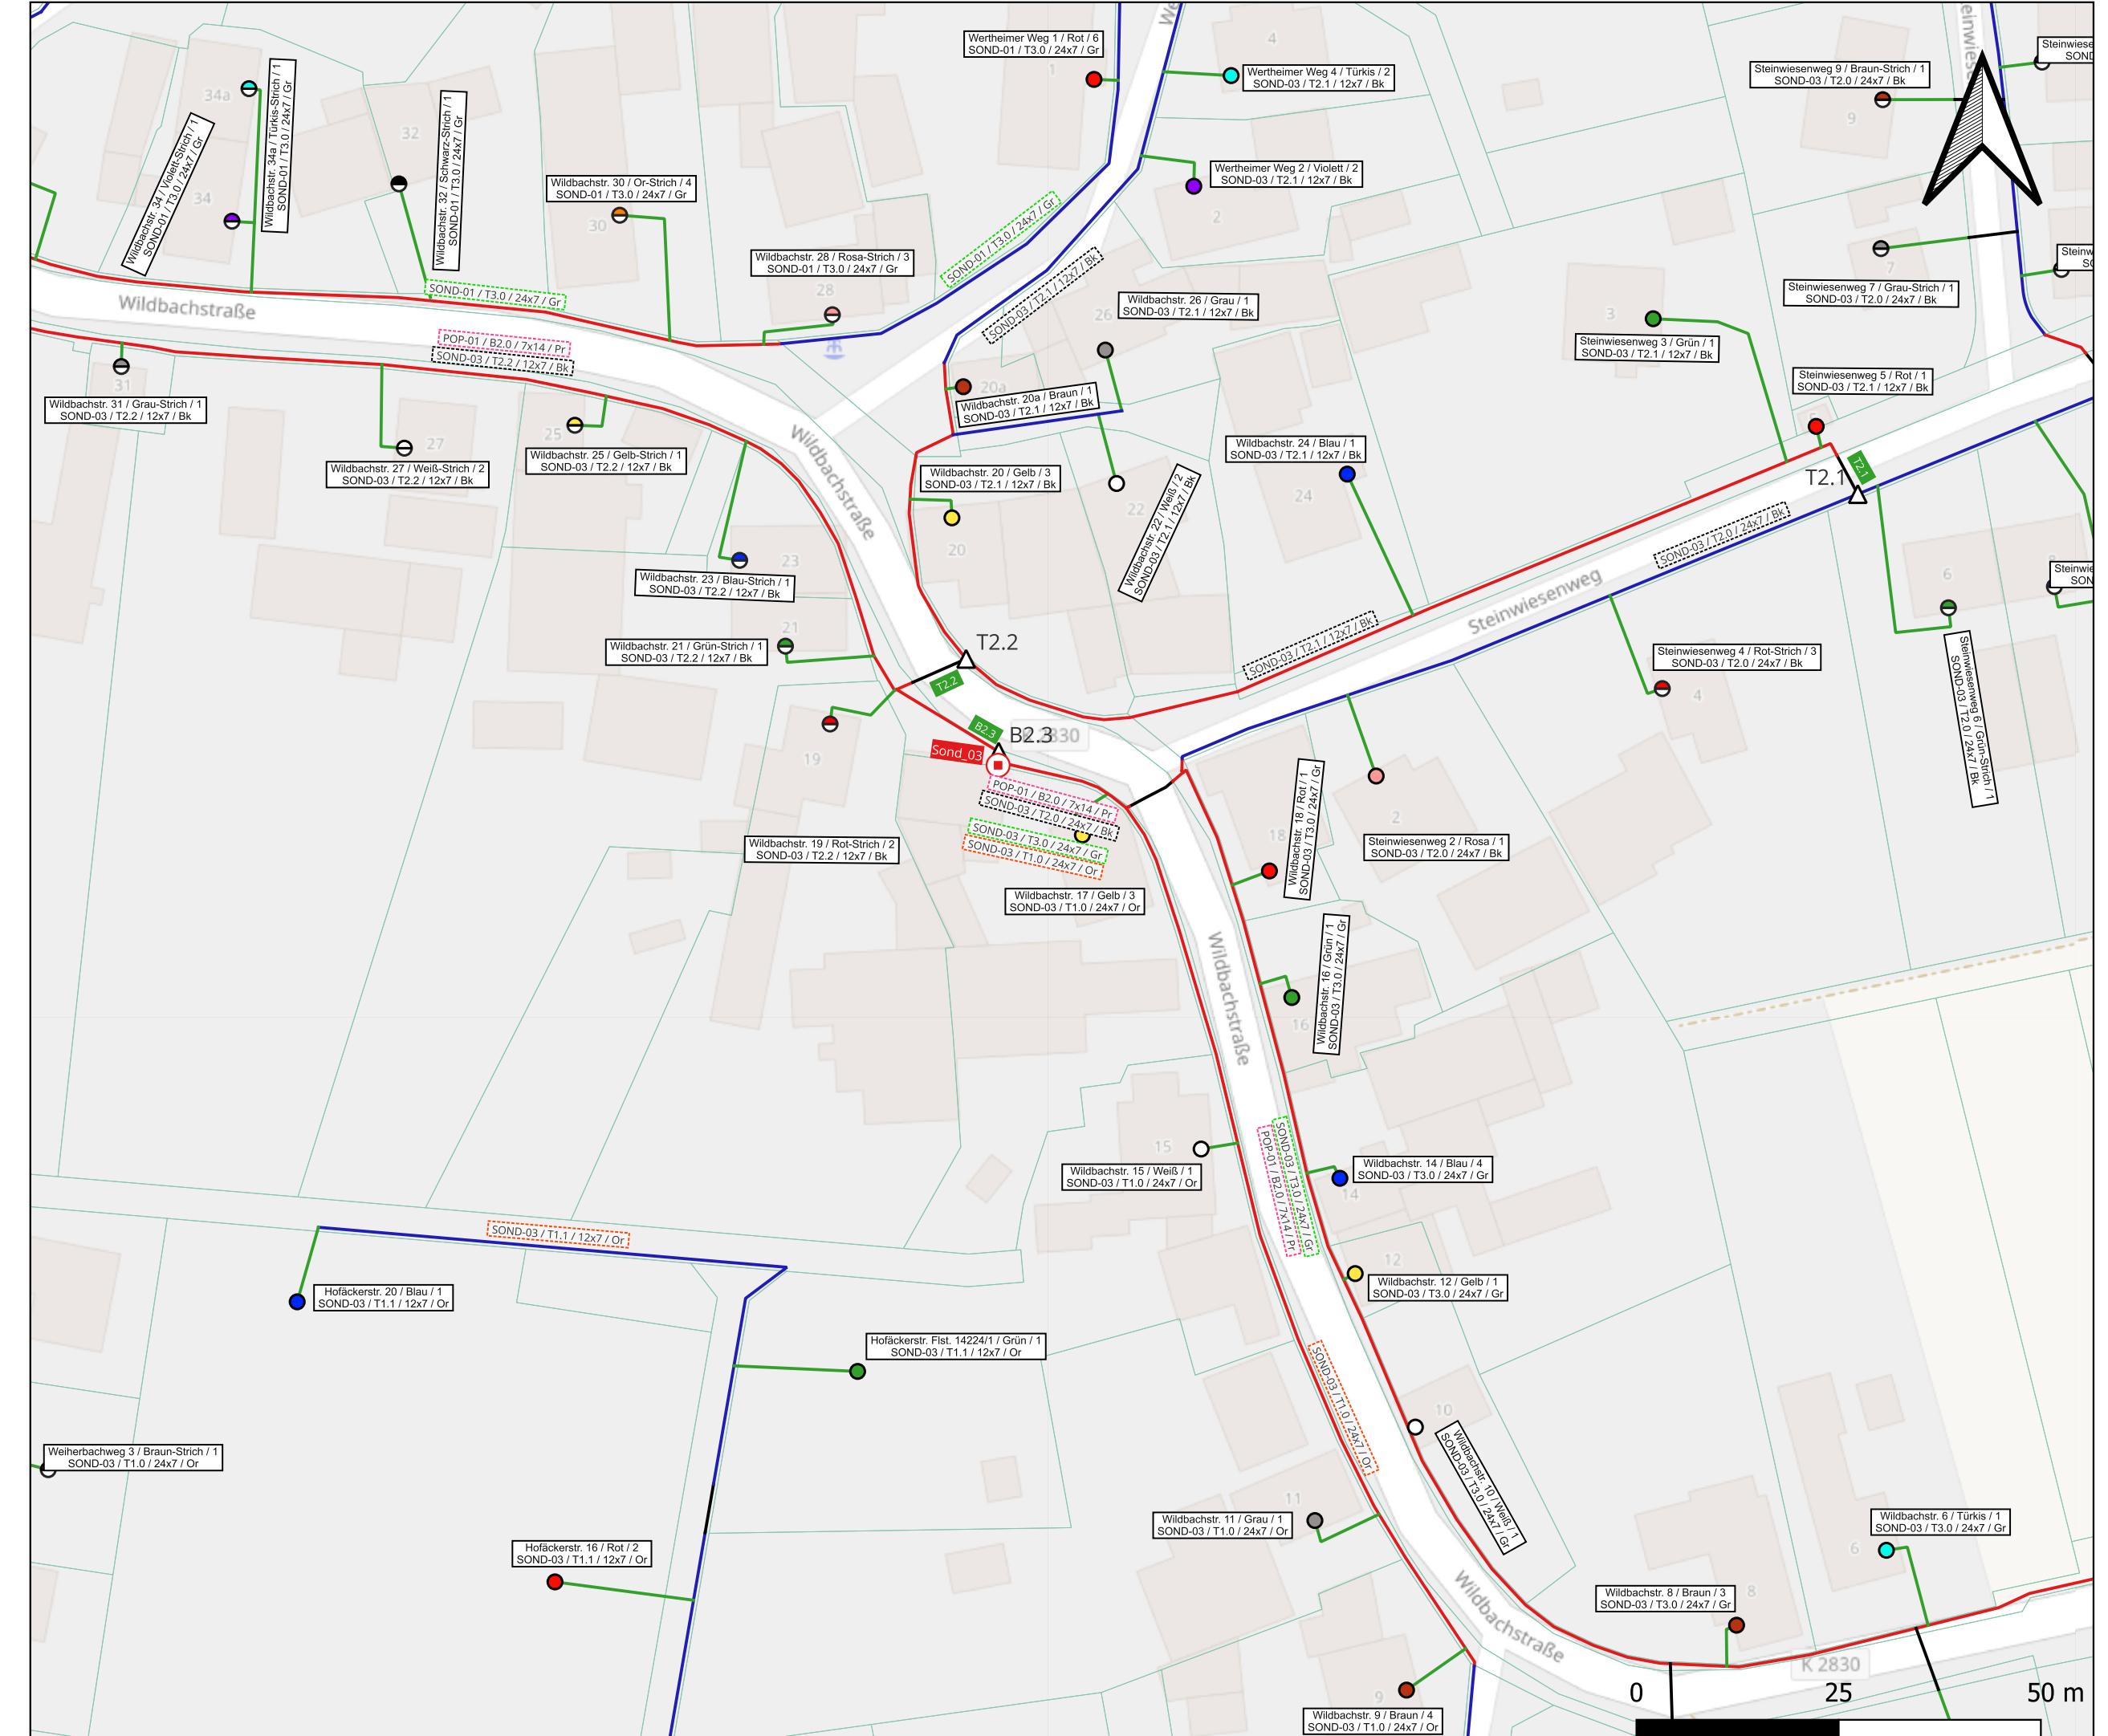

Projekt	Sond
Bearbeiter	Halime Karanfil
Datum	03/04/2025
Blatt	Sond_03 1/4
Massstab	1:750

Legende

□	Manhole
○	Pop
■	Dp
△	Duct_Joint
●	Adresspoint
Trench	
—	Bürgersteig
—	Garden Trench
—	Strasse
—	Strassenkreuzung
—	POP_Cluster
—	Dp_Cluster
—	Flurstck
OpenStreetMap	

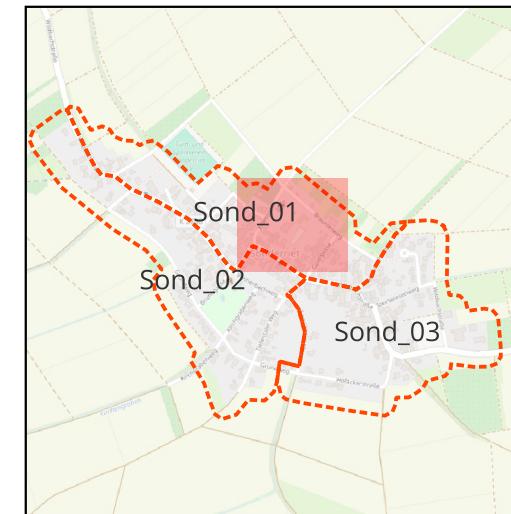

Projekt	Sond
Bearbeiter	Halime Karanfil
Datum	03/04/2025
Blatt	Sond_02 1/4
Massstab	1:750


Legende


- Manhole
 - Pop
 - Dp
 - △ Duct_Joint
 - Adresspoint

Trench

- Bürgersteig
 - Garden Trench
 - Strasse
 - Strassenkreuzung
 - POP_Cluster
 - Dp_Cluster
 - Flurstck

OpenStreetMap

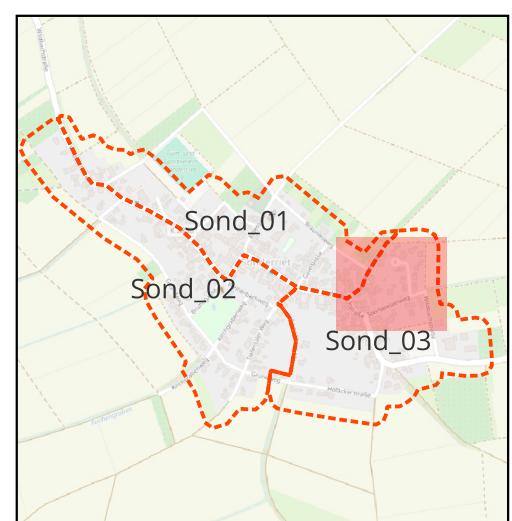

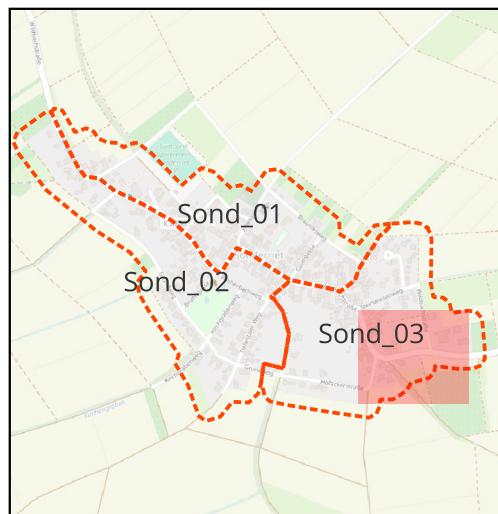

Projekt	Sond
Bearbeiter	Halime Karanfil
Datum	03/04/2025
Blatt	Sond_03 3/4
Massstab	1:750


Legende


- Manhole
- ⊕ Pop
- Dp
- △ Duct_Joint
- Adresspoint

Trench

- Bürgersteig
- Garden Trench
- Strasse
- Strassenkreuzung
- POP_Cluster
- Dp_Cluster
- Flurstck

OpenStreetMap

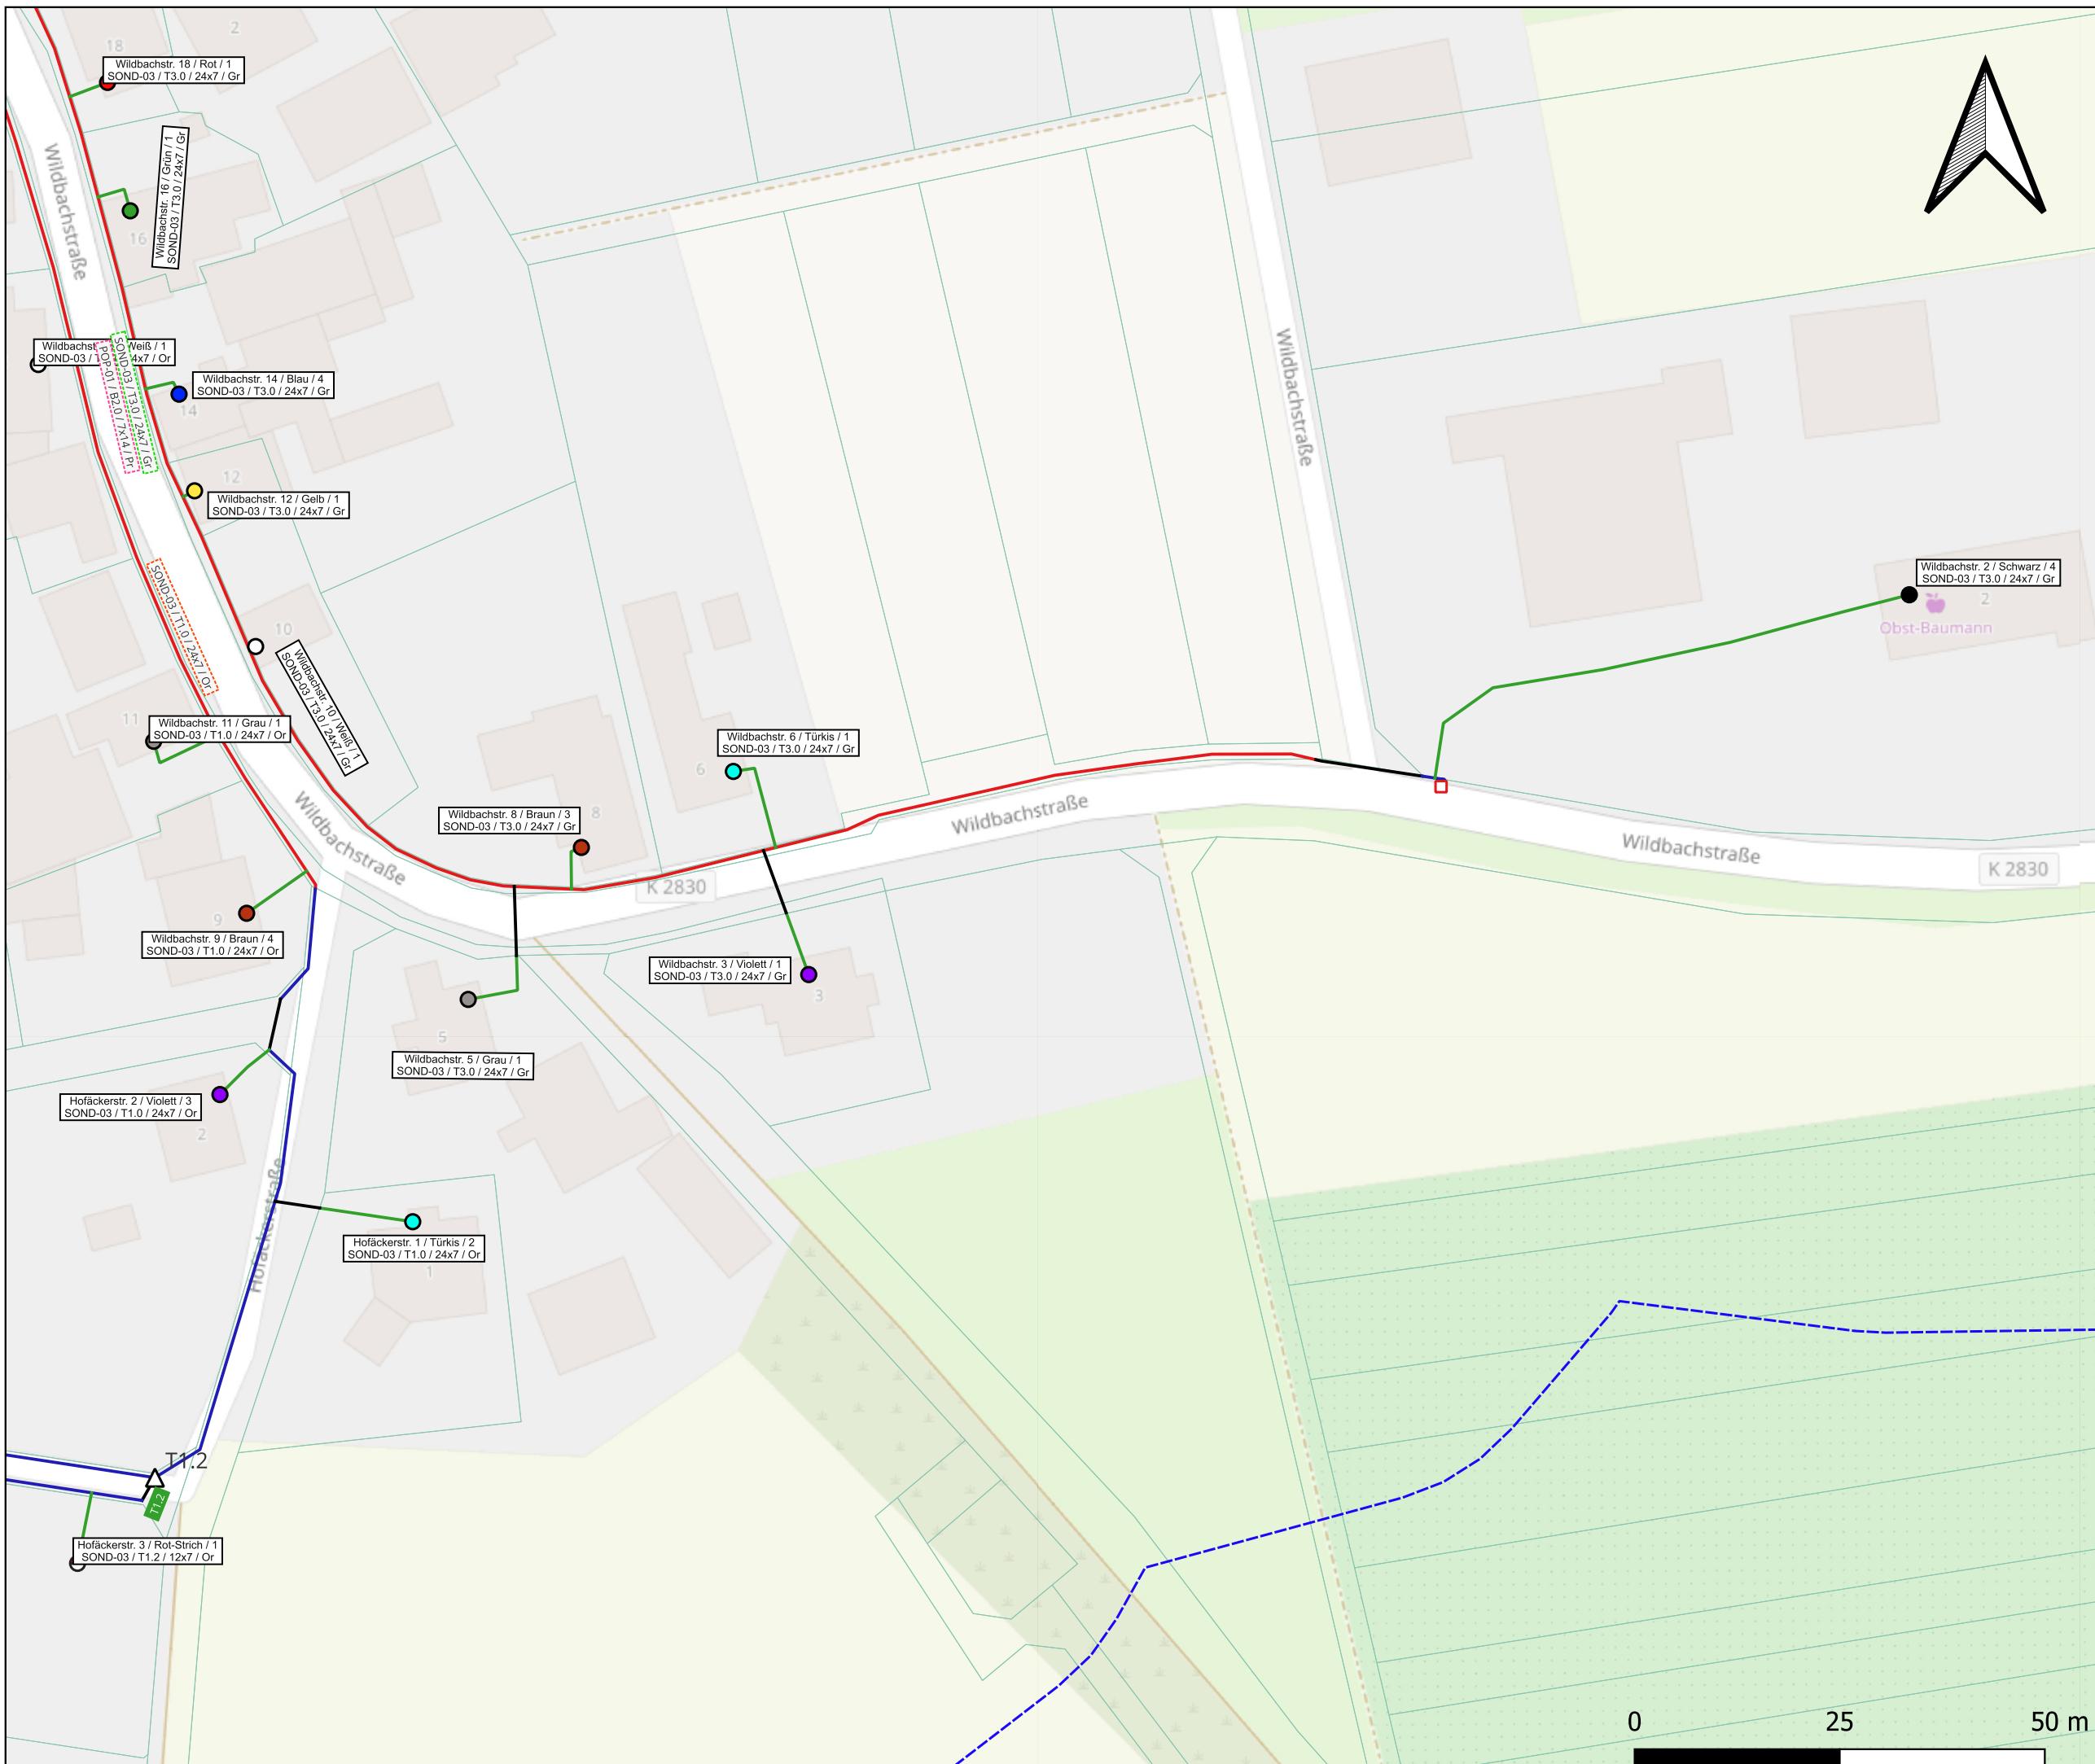

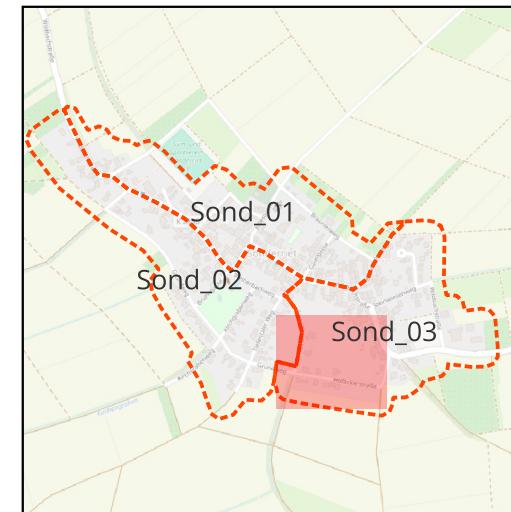

Projekt	Sond
Bearbeiter	Halime Karanfil
Datum	03/04/2025
Blatt	Sond_03 4/4
Massstab	1:750


Legende



- Manhole
- Pop
- Dp
- △ Duct_Joint
- Adresspoint

Trench

- Bürgersteig
- Garden Trench
- Strasse
- Strassenkreuzung
- POP_Cluster
- Dp_Cluster
- Flurstck

OpenStreetMap

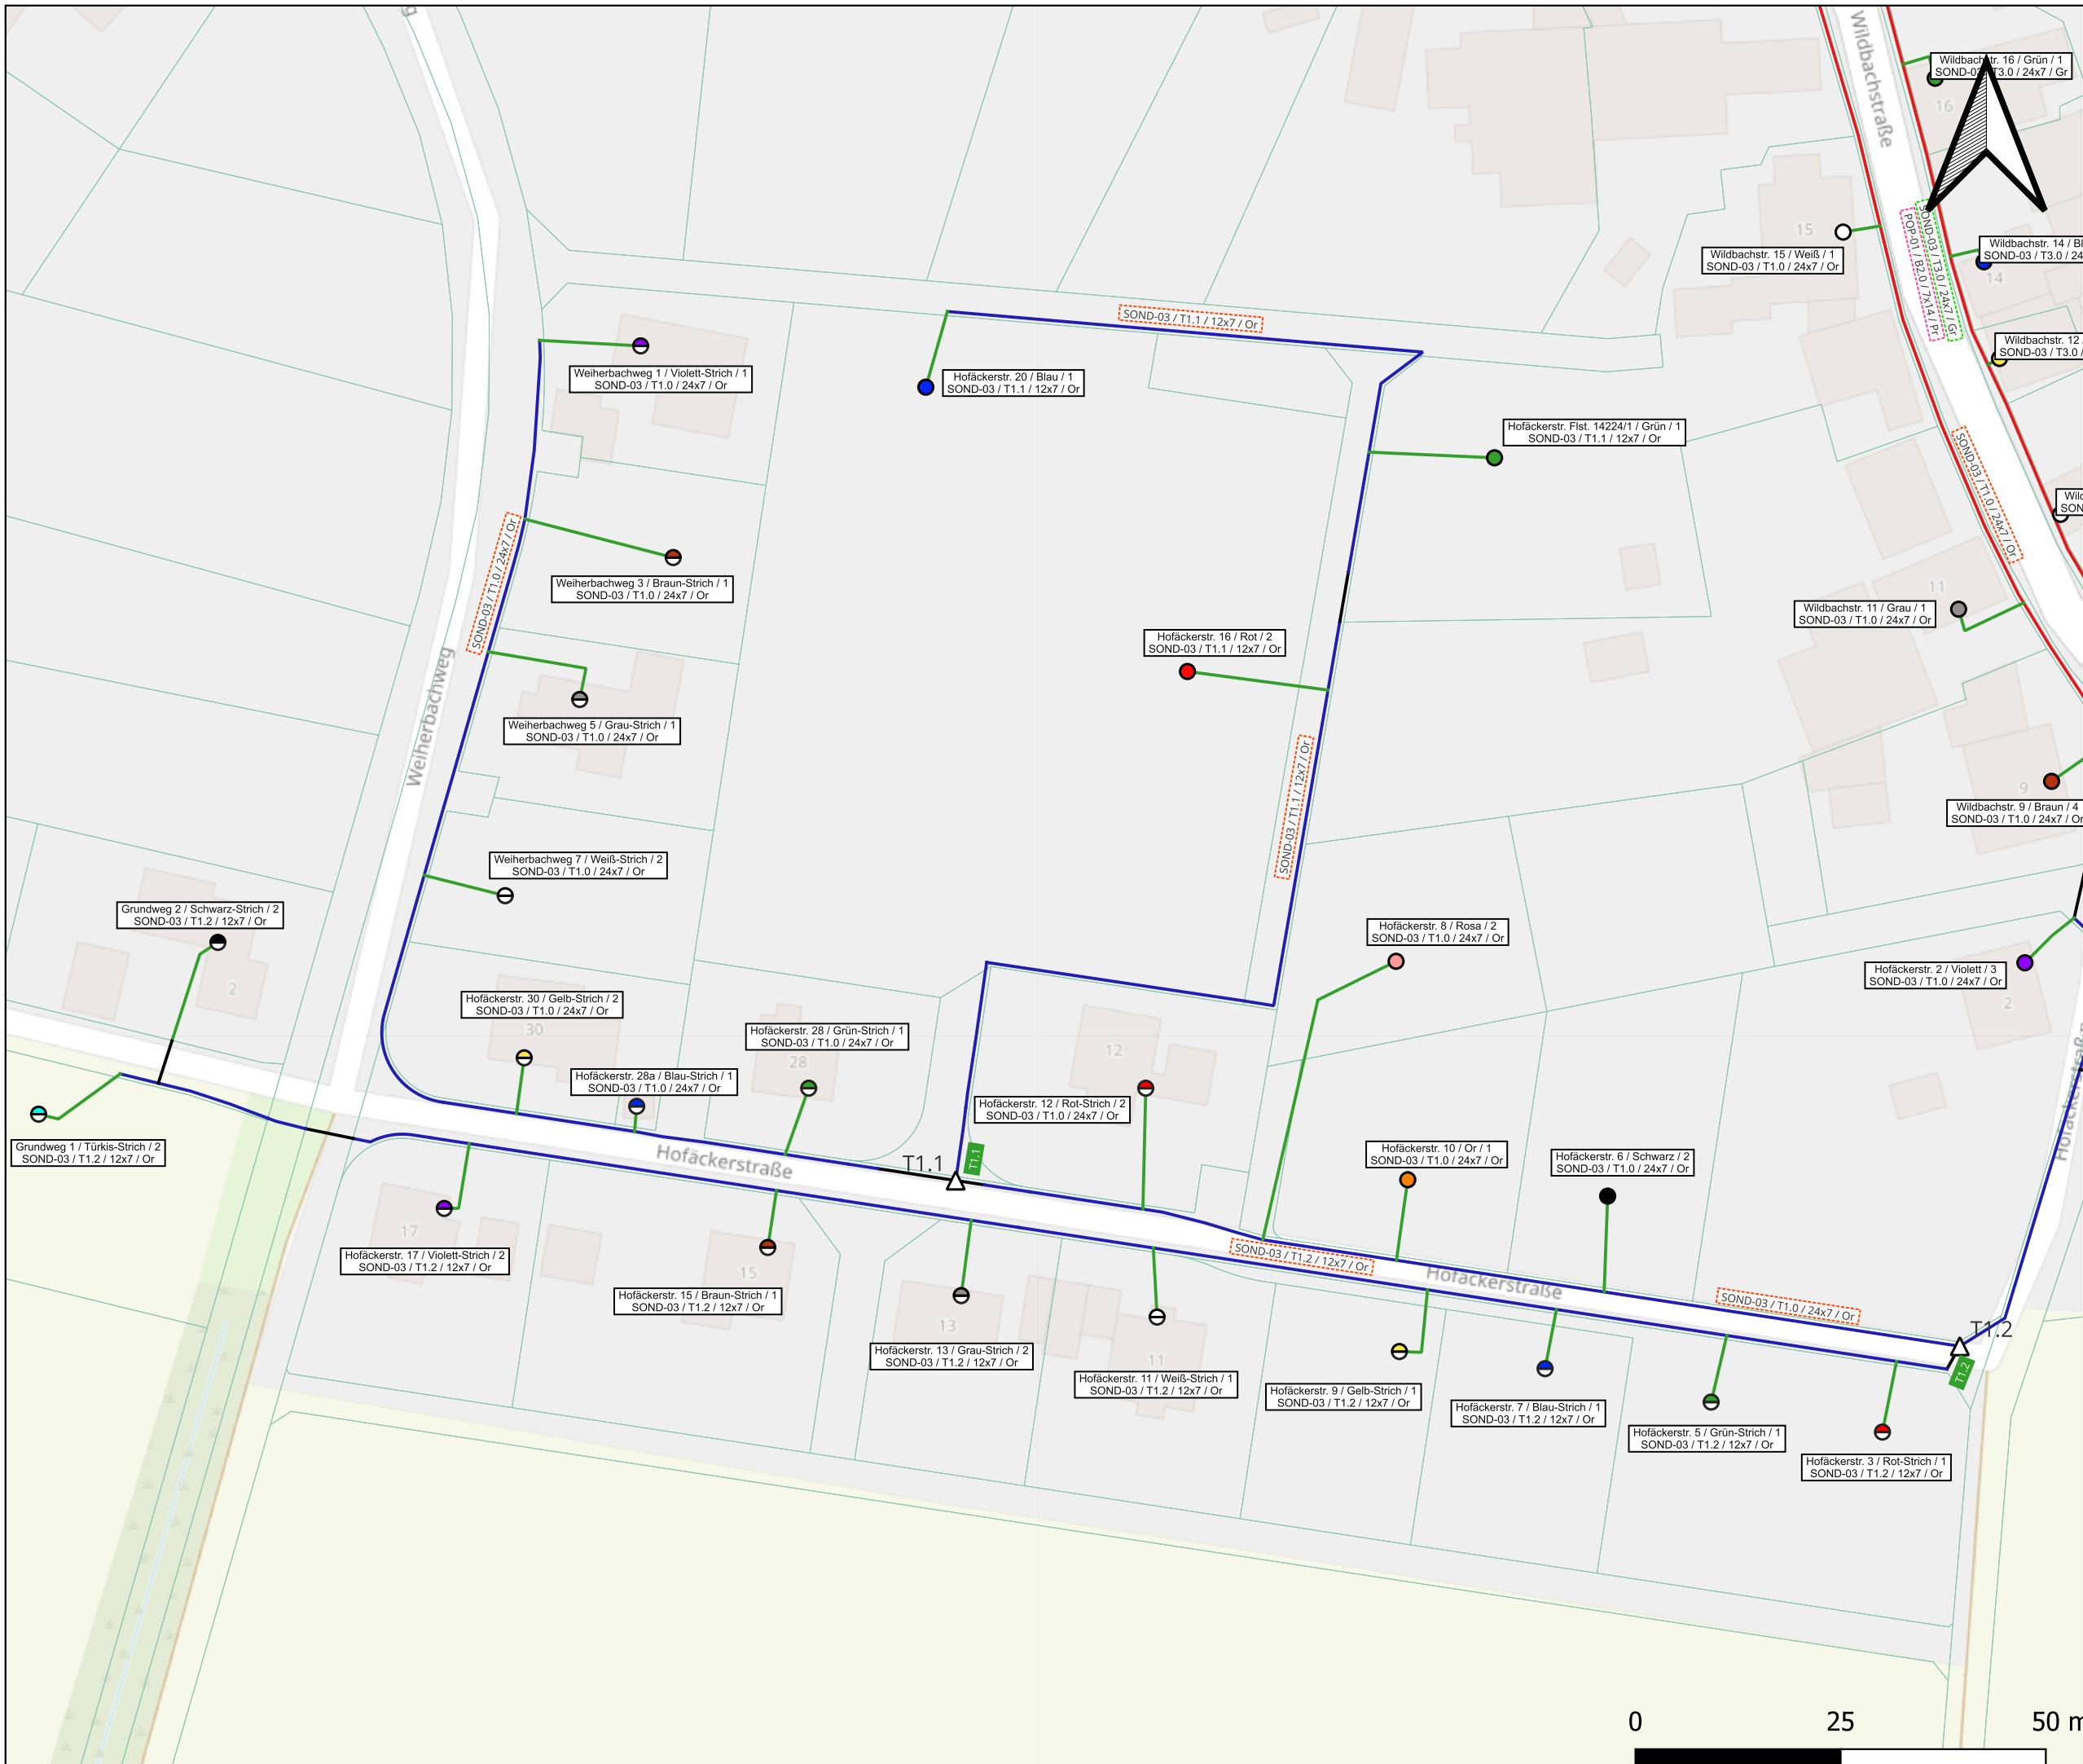

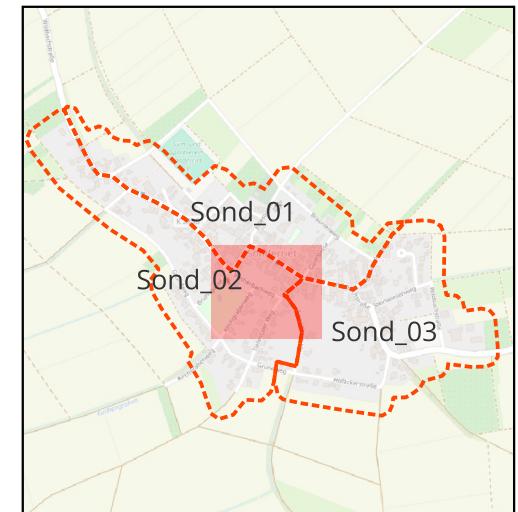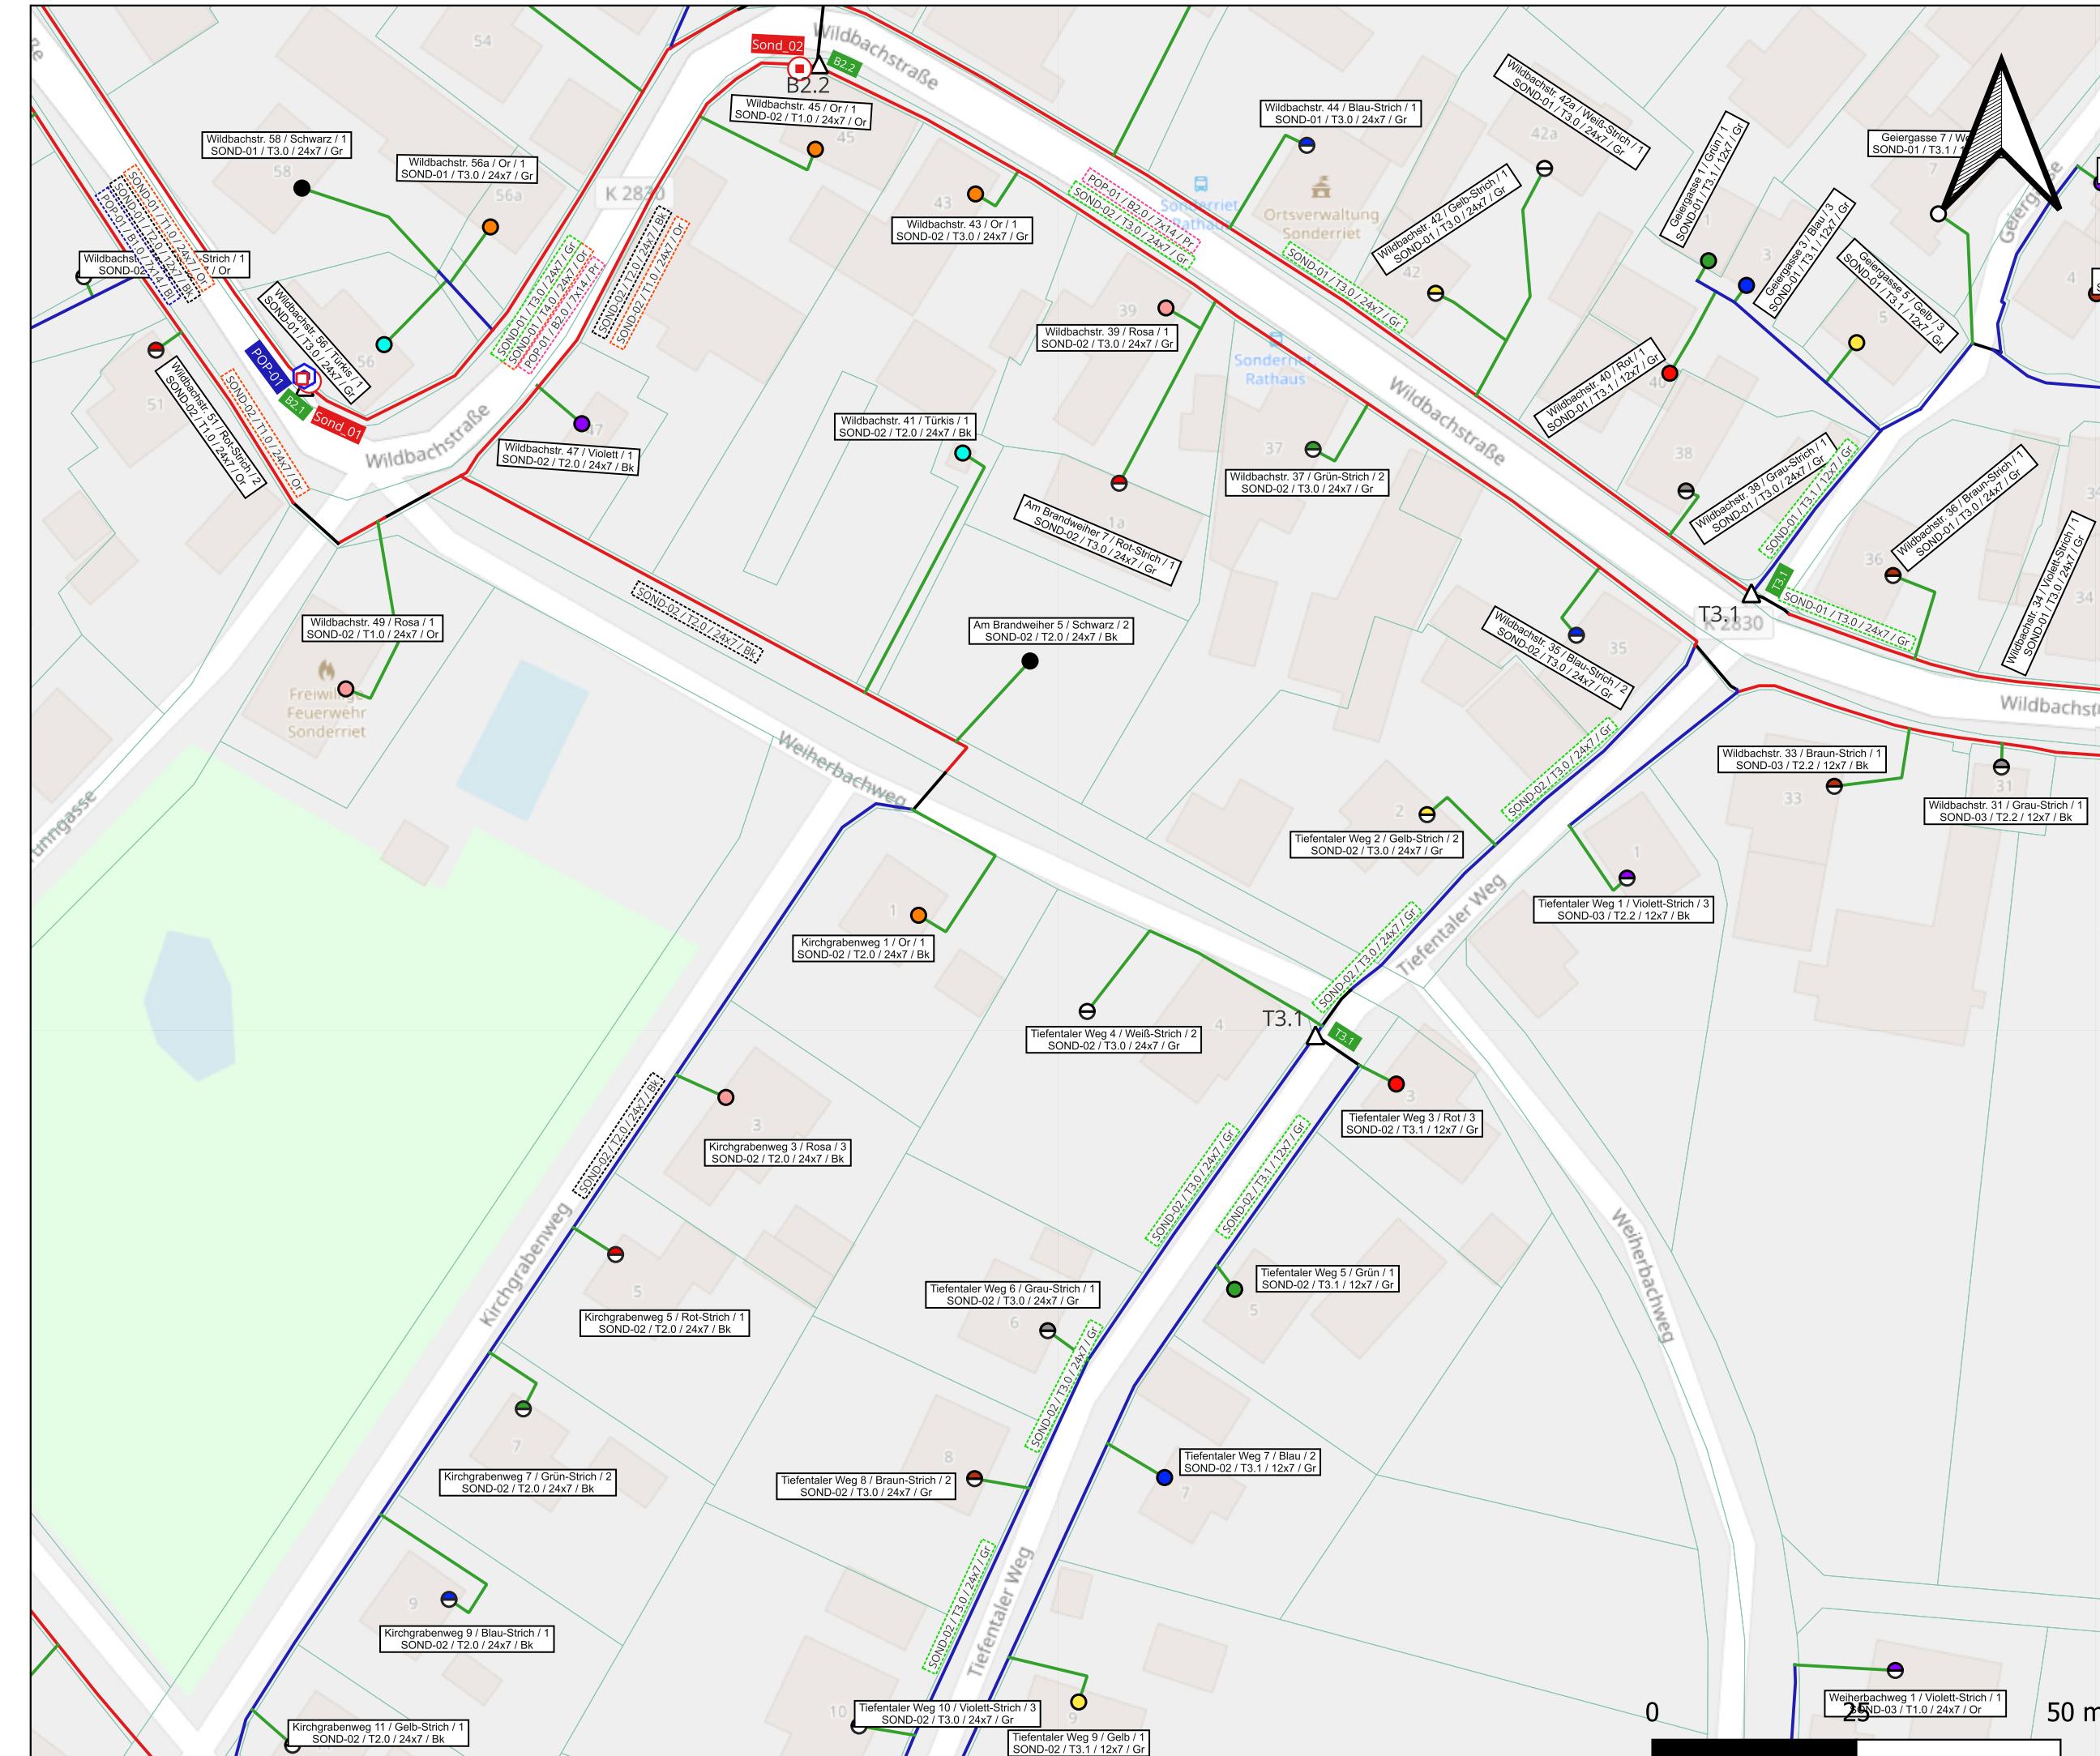

Projekt	Sond
Bearbeiter	Halime Karanfil
Datum	03/04/2025
Blatt	Sond_02 2/4
Massstab	1:750



Legende

- Manhole
- Pop
- Dp
- Duct_Joint
- Adresspoint

Trench

- Bürgersteig
- Garden Trench
- Strasse
- Strassenkreuzung
- POP_Cluster
- Dp_Cluster
- Flurstck

OpenStreetMap

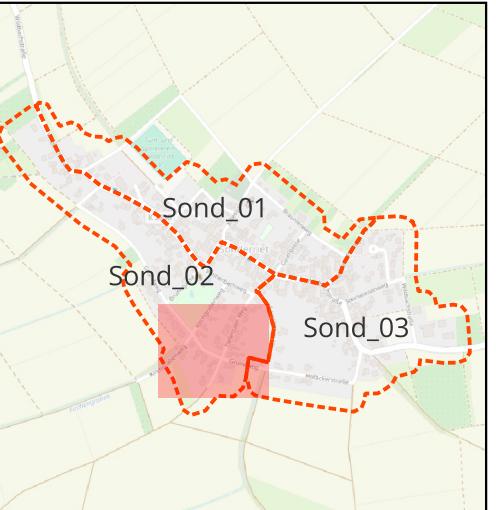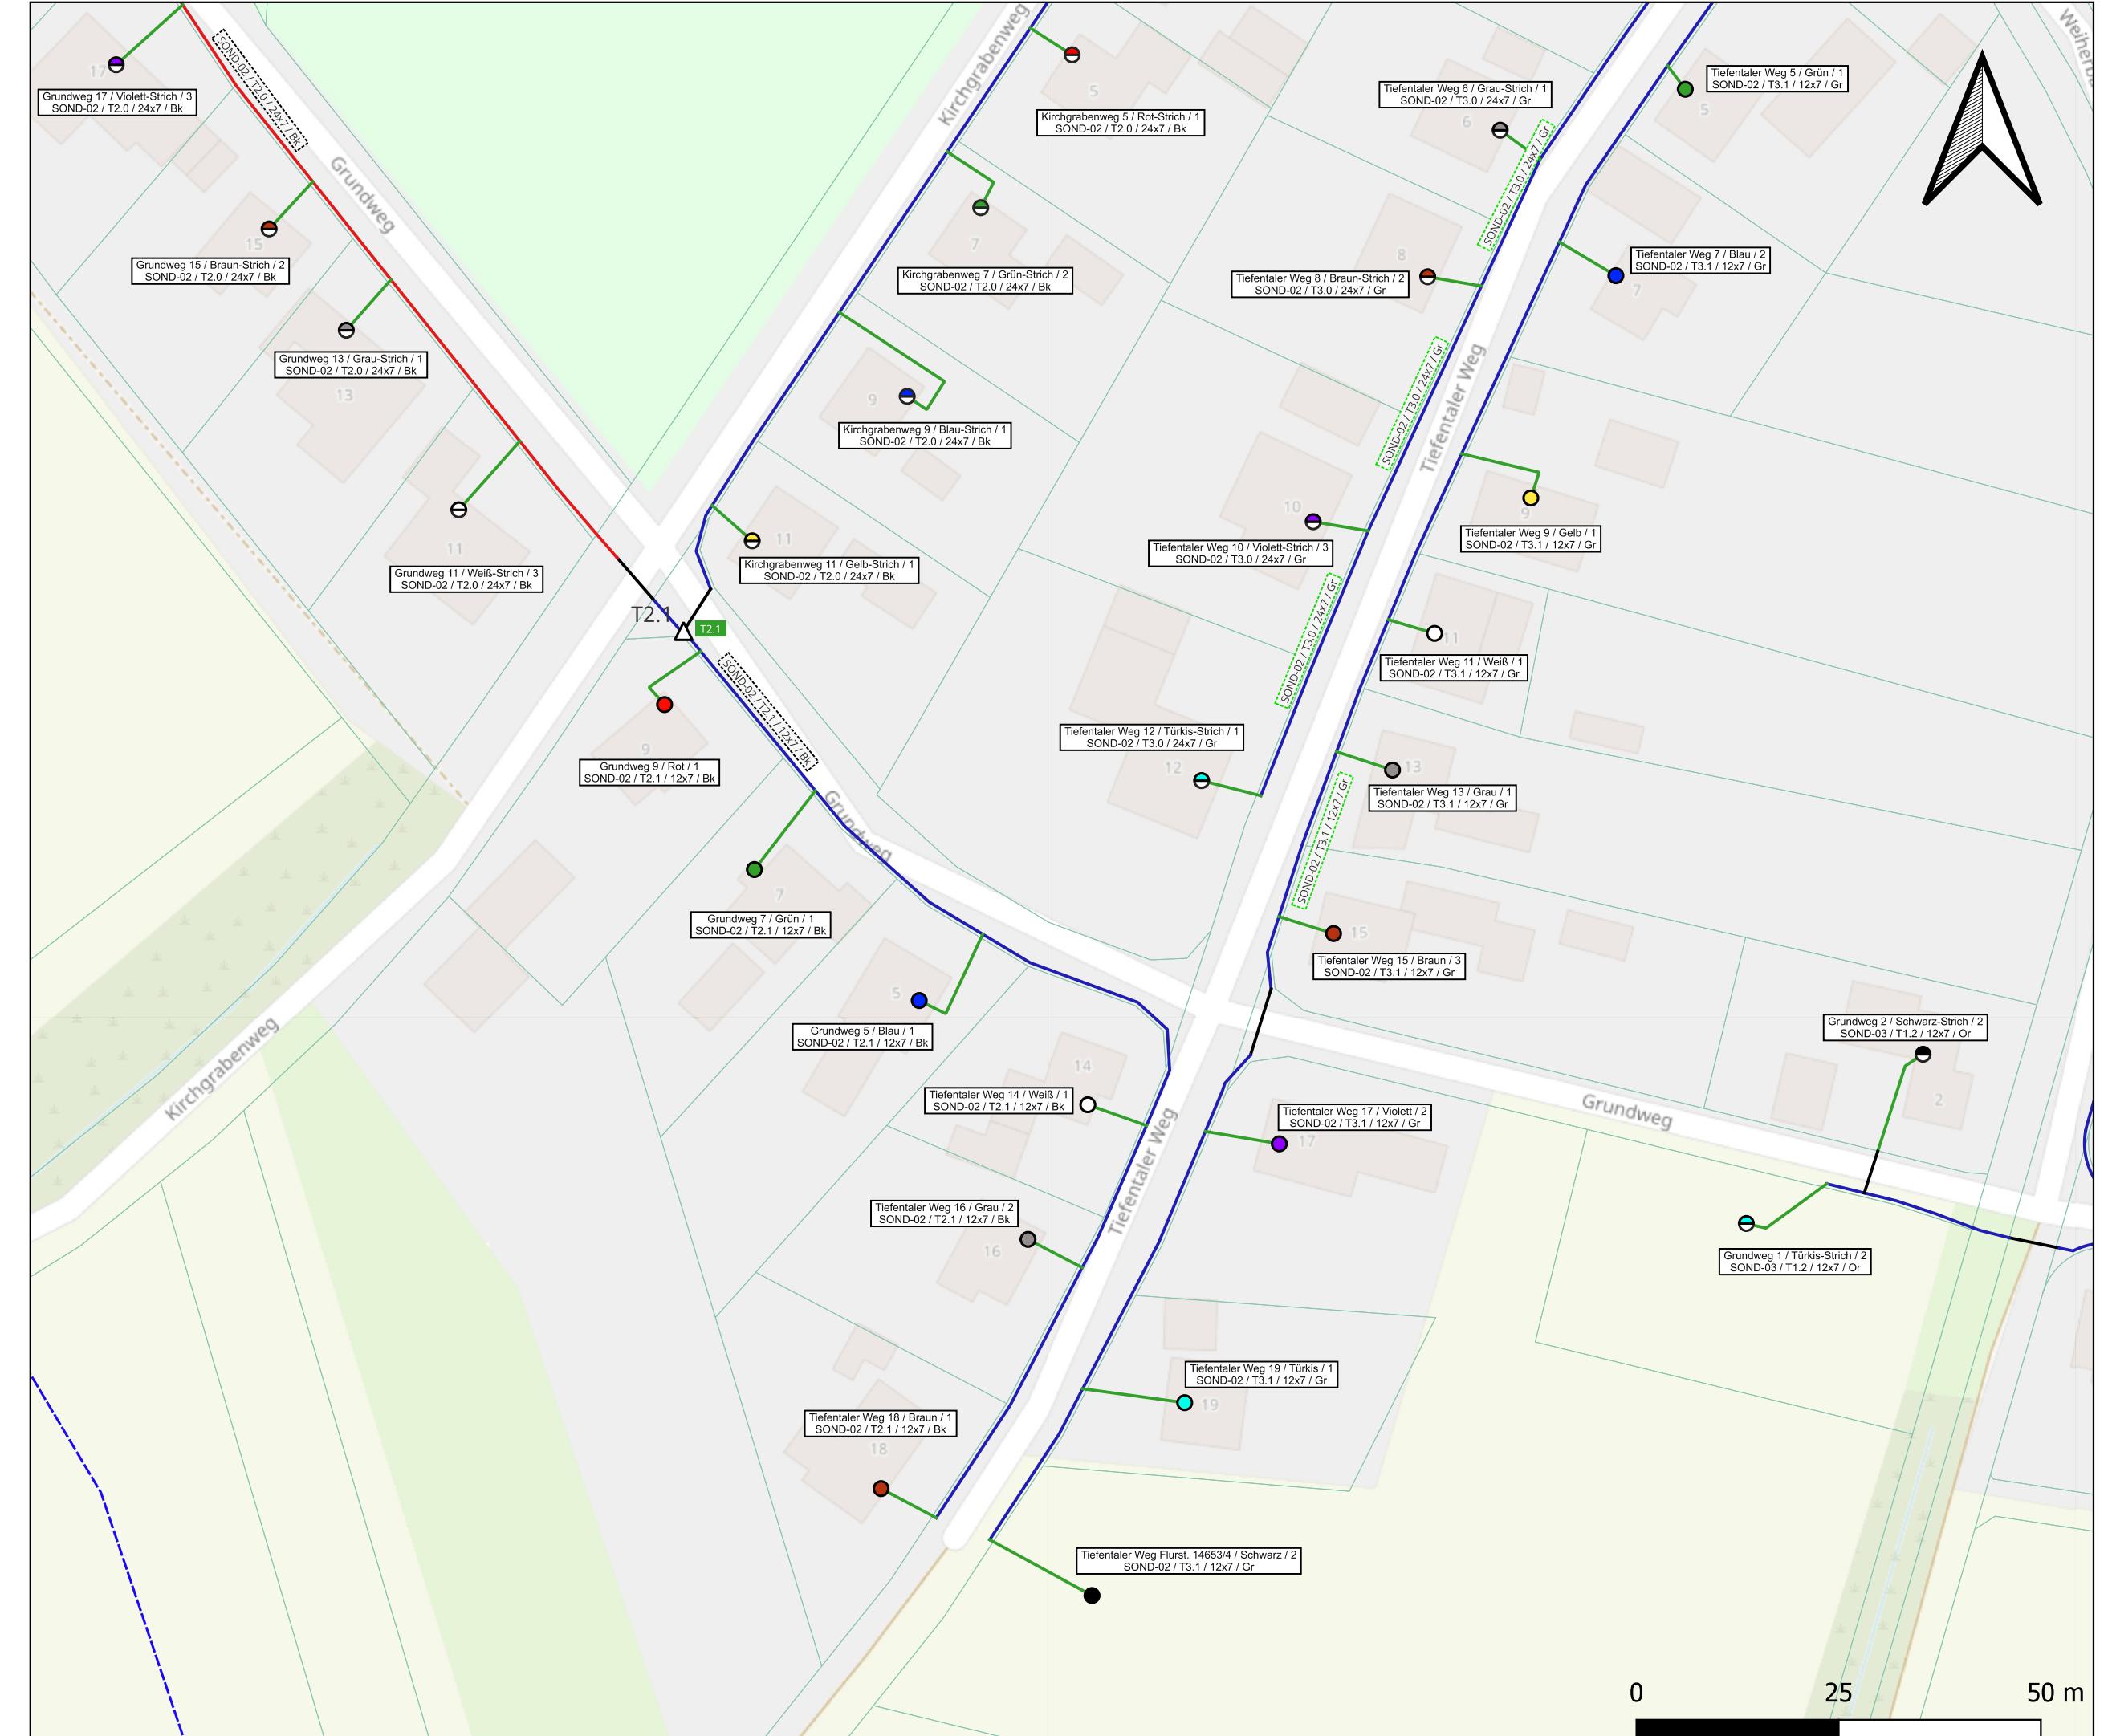

Projekt	Sond
Bearbeiter	Halime Karanfil
Datum	03/04/2025
Blatt	Sond_02 3/4
Massstab	1:750


Legende

- Manhole
- Pop
- Dp
- Duct_Joint
- Adresspoint

Trench

- Bürgersteig
- Garden Trench
- Strasse
- Strassenkreuzung
- POP_Cluster
- Dp_Cluster
- Flurstck

OpenStreetMap

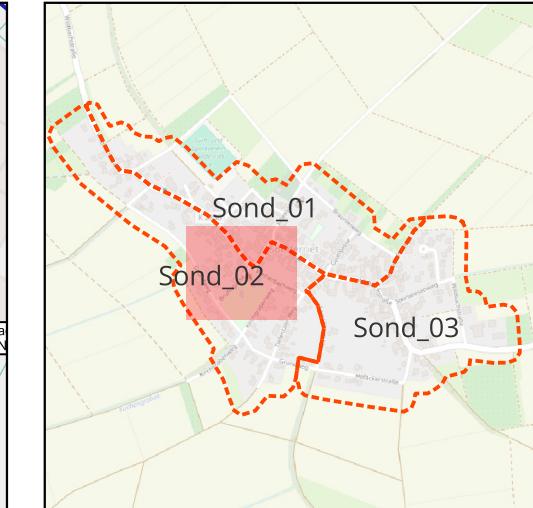

Projekt	Sond
Bearbeiter	Halime Karanfil
Datum	03/04/2025
Blatt	Sond_02 4/4
Massstab	1:750

Legende


- Manhole
- Pop
- Dp
- Duct_Joint
- Adresspoint

Trench

- Bürgersteig
- Garden Trench
- Strasse
- Strassenkreuzung
- POP_Cluster
- Dp_Cluster
- Flurstck

OpenStreetMap




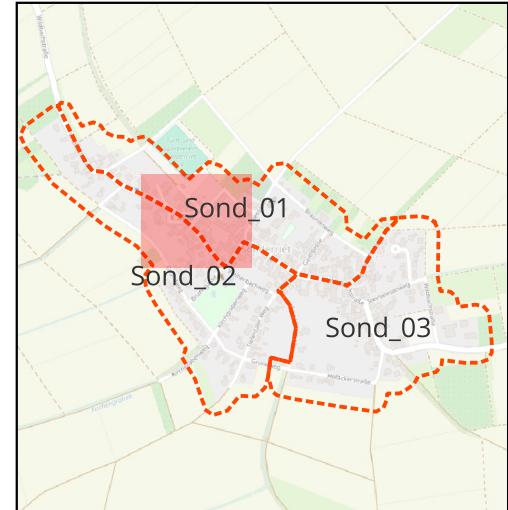

Projekt	Sond
Bearbeiter	Halime Karanfil
Datum	03/04/2025
Blatt	Sond_01 2/4
Massstab	1:750

Legende

□	Manhole
○	Pop
■	Dp
△	Duct_Joint
●	Adresspoint
Trench	
—	Bürgersteig
—	Garden Trench
—	Strasse
—	Strassenkreuzung
□	POP_Cluster
□	Dp_Cluster
□	Flurstck
OpenStreetMap	

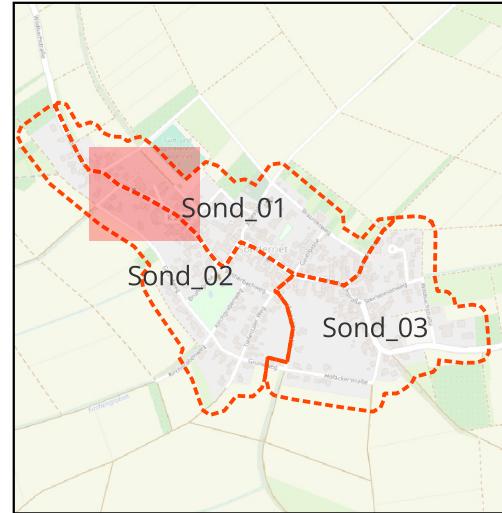

Projekt	Sond
Bearbeiter	Halime Karanfil
Datum	03/04/2025
Blatt	Sond_01 3/4
Massstab	1:750

Legende



- Manhole
- Pop
- Dp
- △ Duct_Joint
- Adresspoint

Trench

- Bürgersteig
- Garden Trench
- Strasse
- Strassenkreuzung
- POP_Cluster
- Dp_Cluster
- Flurstck

OpenStreetMap



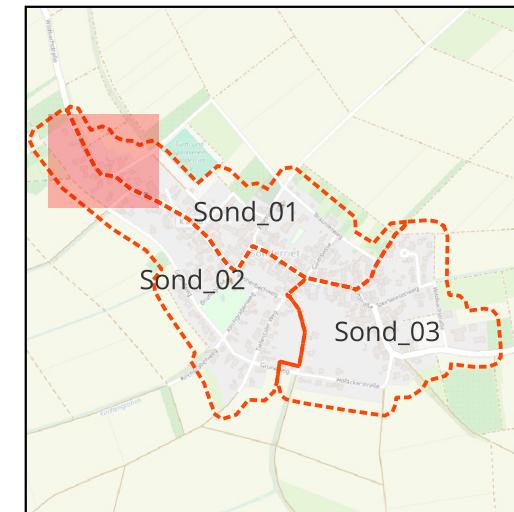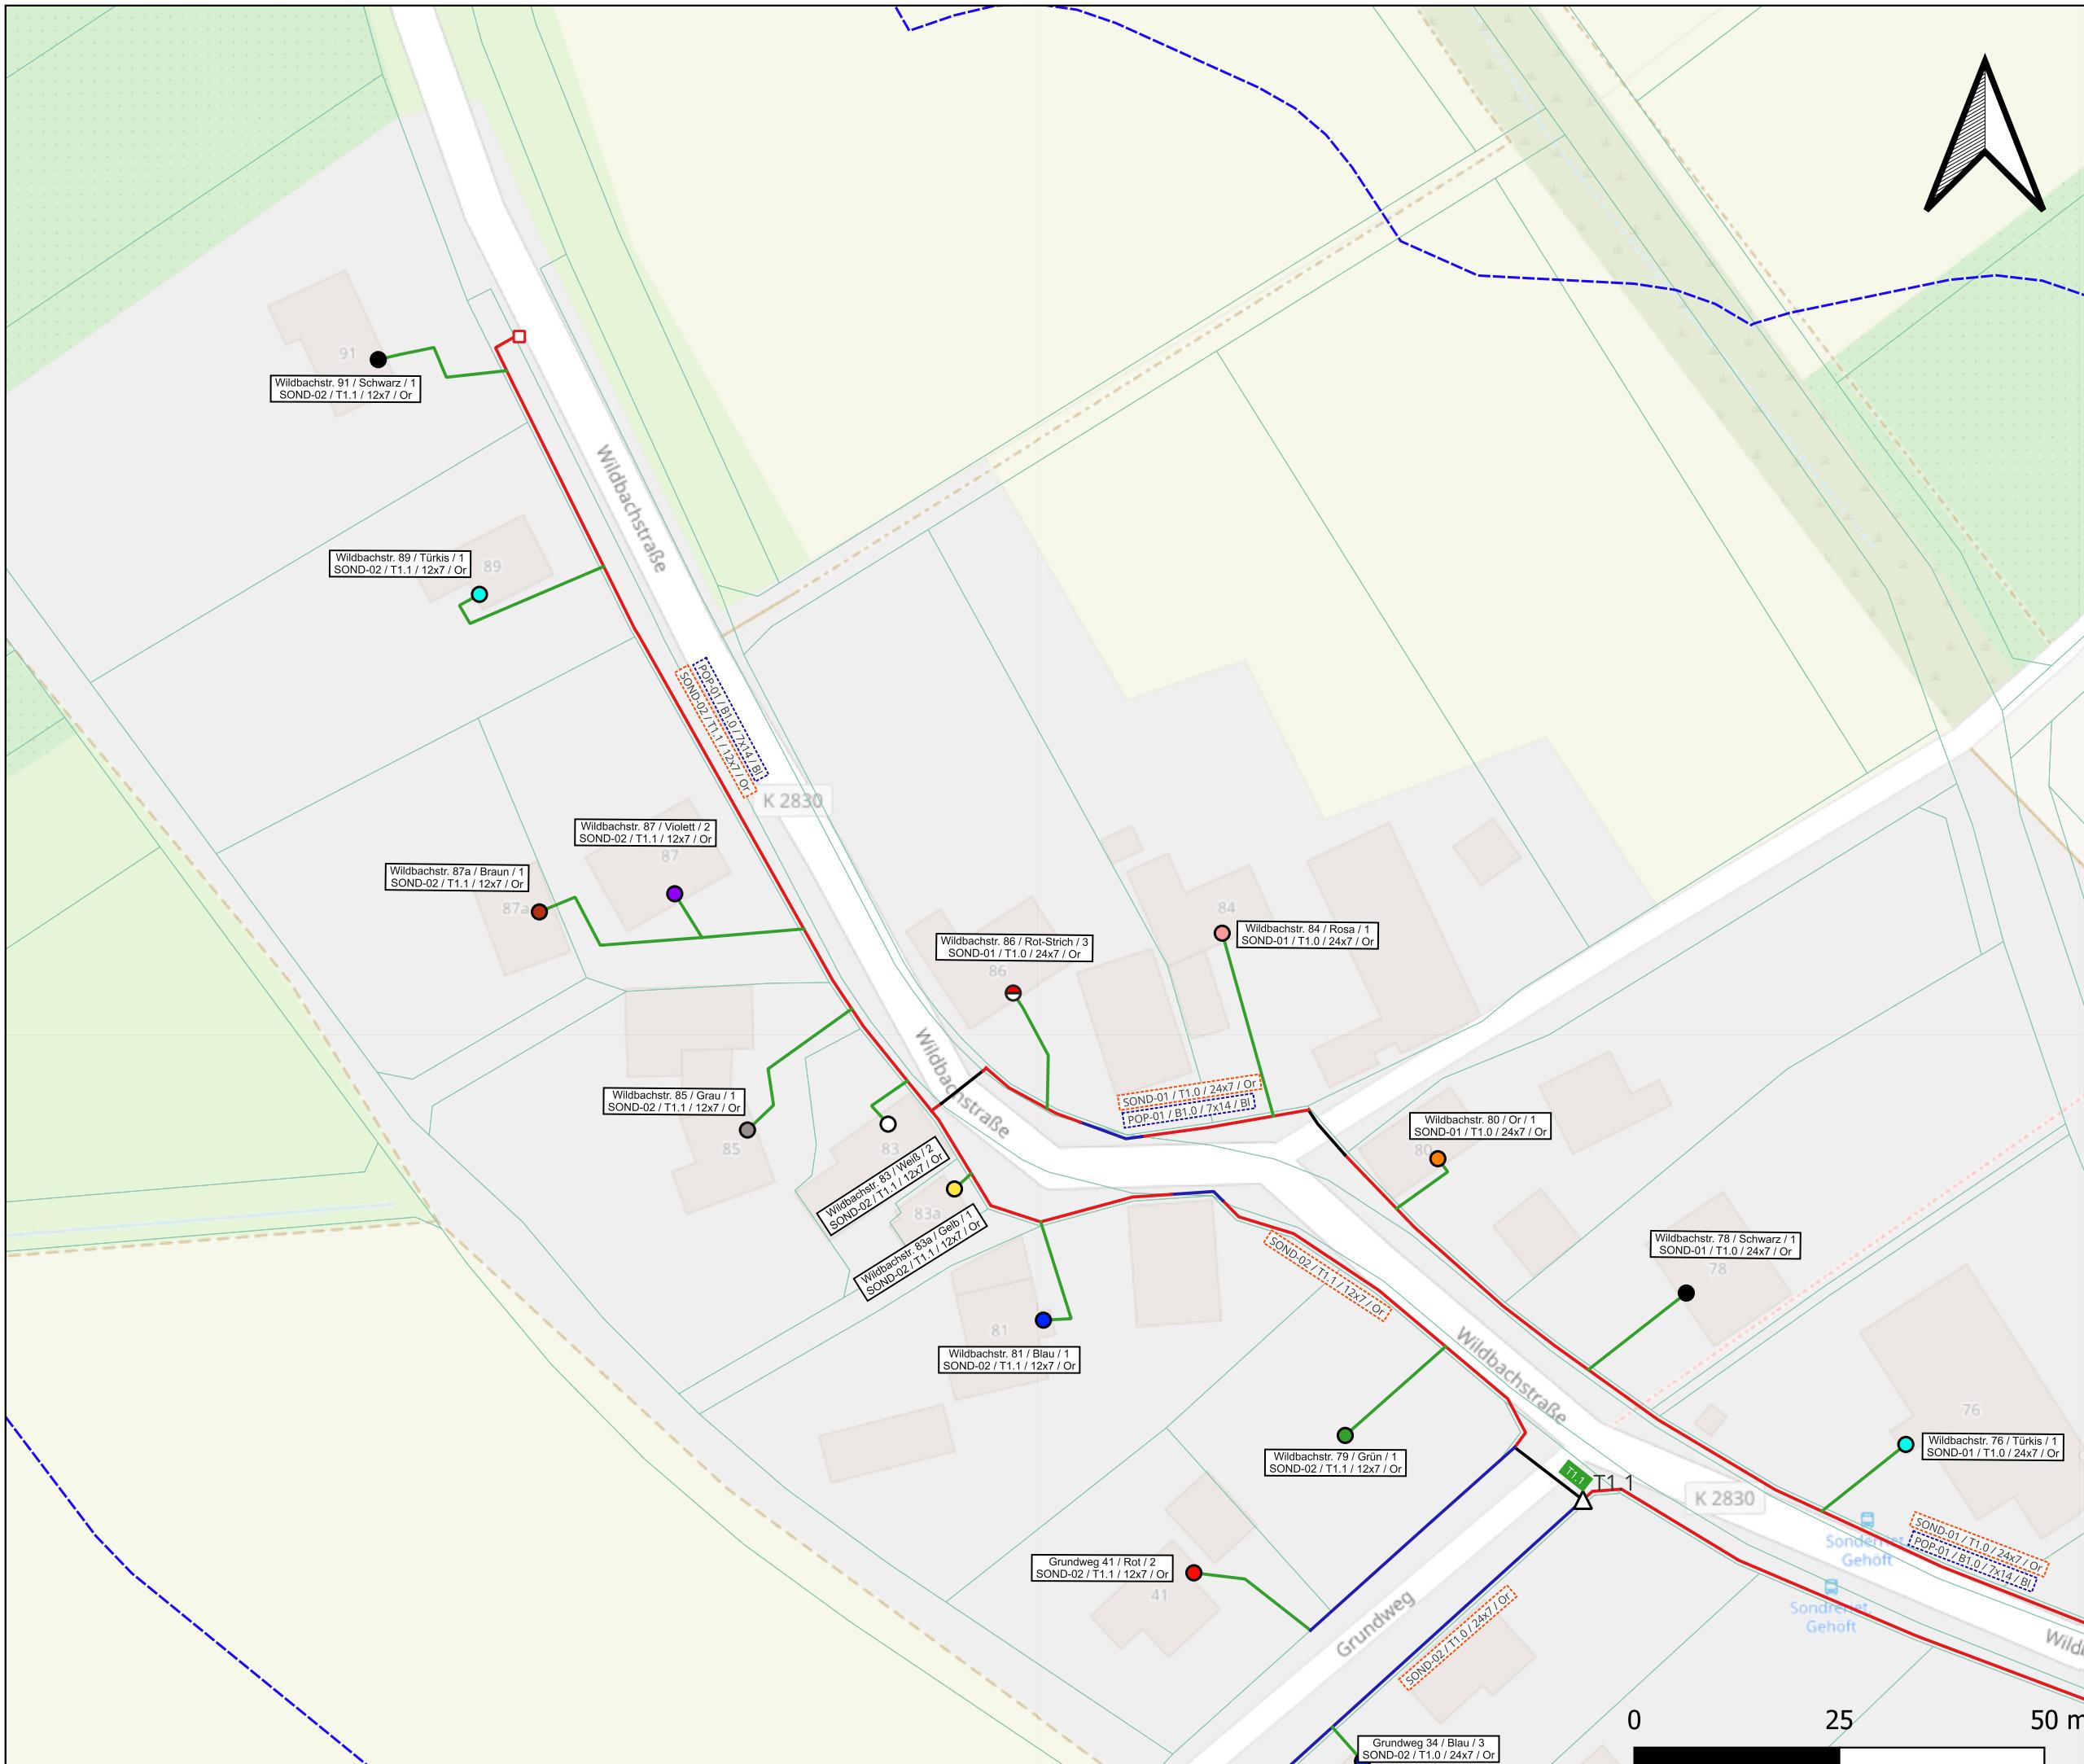

Projekt	Sond
Bearbeiter	Halime Karanfil
Datum	03/04/2025
Blatt	Sond_01 4/4
Massstab	1:750

Legende

- Manhole
- Pop
- Dp
- Duct_Joint
- Adresspoint
- Trench
 - Bürgersteig
 - Garden Trench
 - Strasse
 - Strassenkreuzung
 - POP_Cluster
 - Dp_Cluster
 - Flurstck
- OpenStreetMap